

DJ

PORTFOLIO • 2026

Deepanshu Jindal

Architect and **building information modelling** specialist.

Council of Architecture Reg. no. CA/2024/171712

deepanshujindal.com • connect@deepanshujindal.com



Broadway Junction Station Complex

An ADA upgrade and circulation improvements at the interchange where the A/C, J/Z and L subway lines meet. New elevators, transfer bridges and an expanded control house make every line step-free.

FIRM	AtkinsRéalis, Transport Architecture (USA)
OWNER	MTA Construction & Development
CONTRACT	A37130
VALUE	US\$500 million, funded by the U.S. Department of Transportation
ROLE	Graduate Architect, core architecture team



PROPOSED WORKS: ELEVATORS EL-1 TO EL-7, A/C-L TRANSFER BRIDGE, FOOTBRIDGE TO THE J/Z CONCOURSE, CONTROL HOUSE EXPANSION




BROADWAY JUNCTION • VISUALISATION

Entrance through the expanded control house




BROADWAY JUNCTION • VISUALISATION

Inside the control house: new elevators, escalators and the staircase up to the L-line bridge

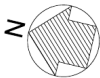

+

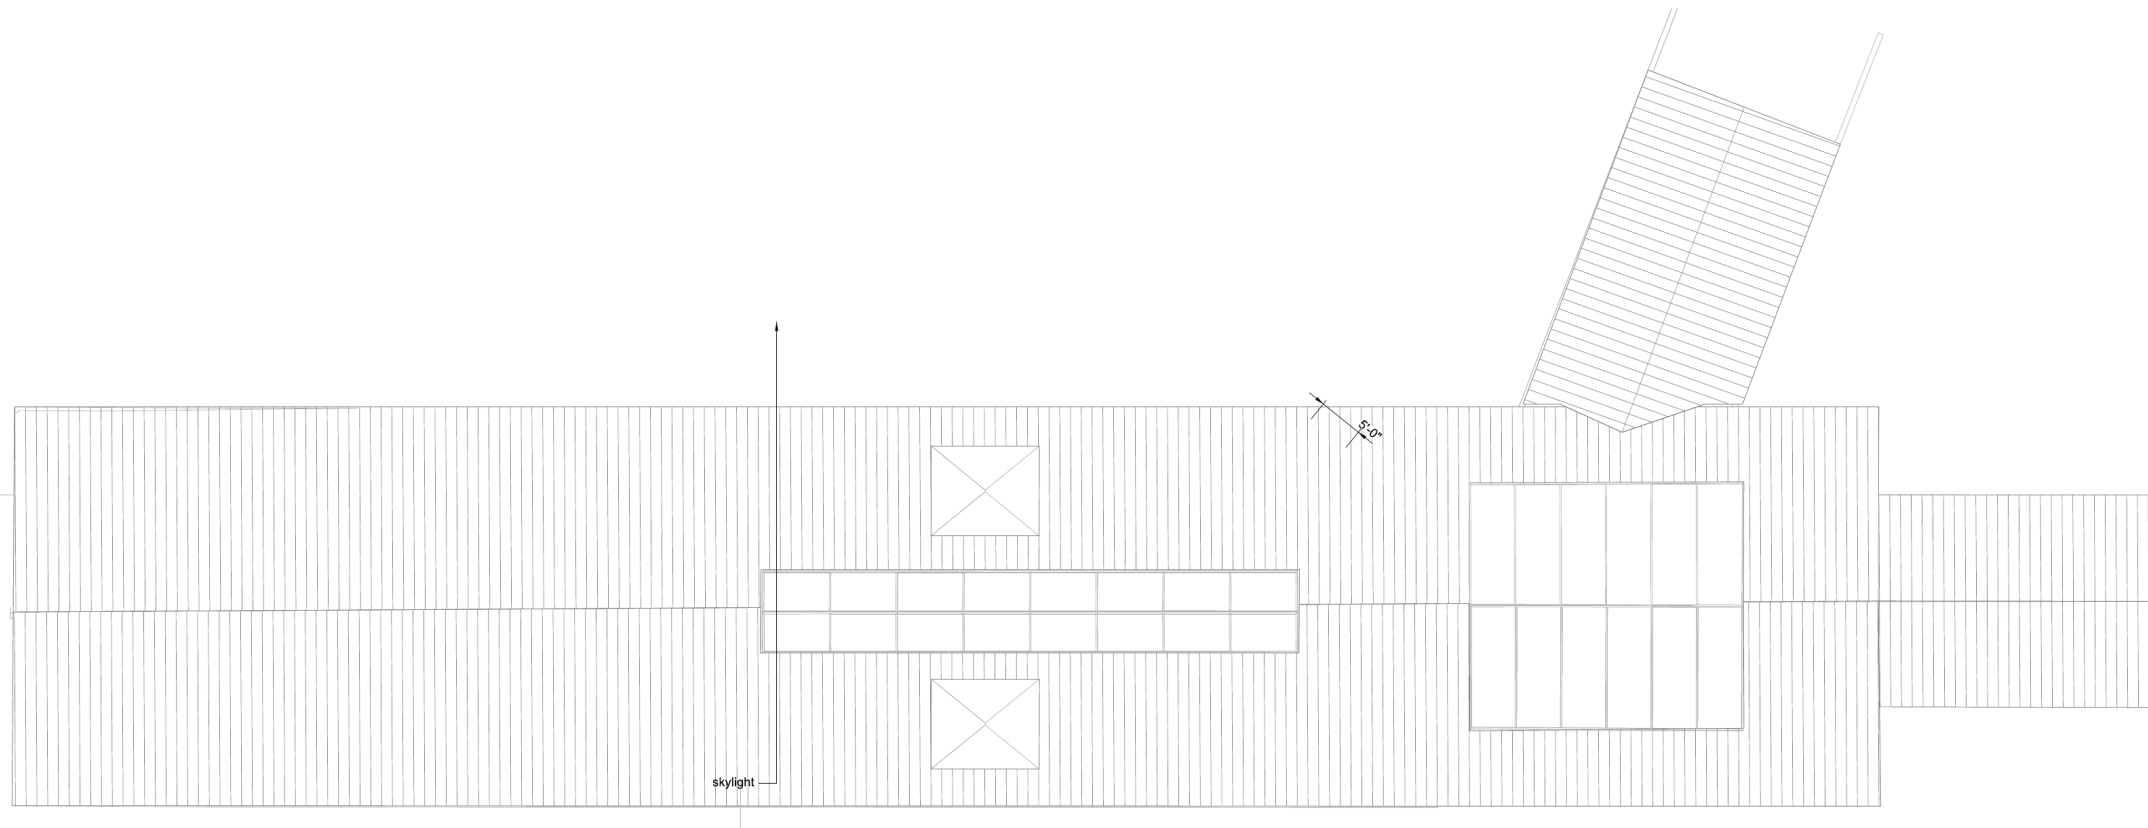

Note:
Structures to provide existing and proposed structural columns and frameworks

IT IS A VIOLATION OF THE PROFESSIONAL LICENSE LAW FOR ANY PERSON TO ALTER THIS DRAWING IN ANY WAY, UNLESS ACTING UNDER THE DIRECTION OF A LICENSED PROFESSIONAL ENGINEER / REGISTERED ARCHITECT. THE ALTERING ENGINEER/ARCHITECT SHALL AFFIX TO THE DRAWING HIS/HER SEAL AND THE NOTATION "ALTERED BY" FOLLOWED BY HIS/HER SIGNATURE AND THE DATE OF SUCH ALTERATION AND A SPECIFIC DESCRIPTION OF THE ALTERATION.			
-	-	-	-
-	-	-	-
-	-	-	-
-	-	-	-
REVISION	DESCRIPTION	DATE	APPROVED

REVISIONS



CONSTRUCTION
& DEVELOPMENT




10 E 40TH STREET
NEW YORK NY, 10016

CONTRACT A37130
ADA UPGRADE OF BROADWAY JUNCTION STATION COMPLEX &
CIRCULATION IMPROVEMENTS, BOROUGH OF BROOKLYN

L STATION PROPOSED
STREET LEVEL GENERAL
ARRANGEMENT PLAN

DRAWN BY	VINODHINI	15 FEBRAURY 2024	DATE: 15 FEBRAURY 2024
DESIGNED BY	WALDO MAFFEI	-	ARCHITECTURE
CHECKED BY	-	-	DRAWING NO: A37130_A-102001
APPROVED BY	-	-	REVISION

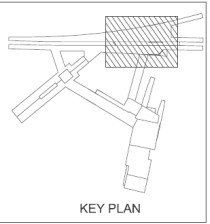

CONSTRUCTION DOCUMENTS


L Station:
proposed street-
level general
arrangement
plan

Part of the architectural drawing set
for Contract A37130, prepared to
MTA Construction & Development
standards with the AtkinsRéalis US
team.


J/Z Station: transverse and longitudinal sections

Sections through the J/Z station from base of rail to roof, showing the platform and mezzanine levels and the new vertical circulation.


Drawn by Deepanshu Jindal, February 2024.

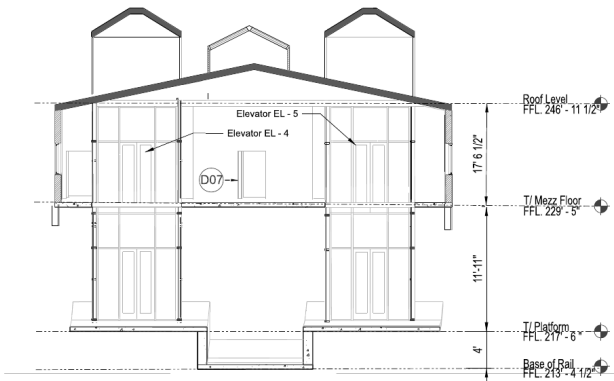


1 J/Z STATION - TRASVERSE SECTION
1/8" = 1'-0"

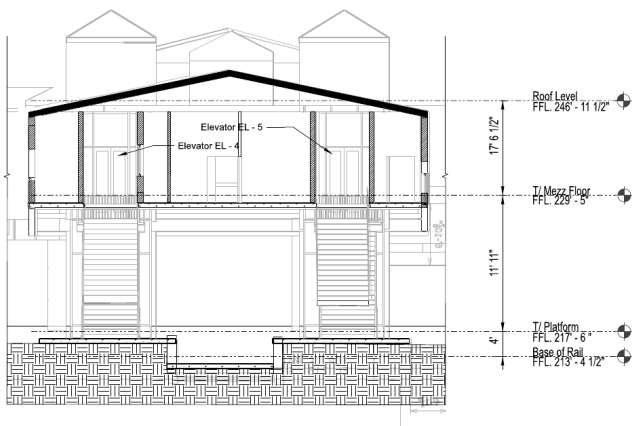

2 J/Z STATION - TRASVERSE SECTION
1/8" = 1'-0"

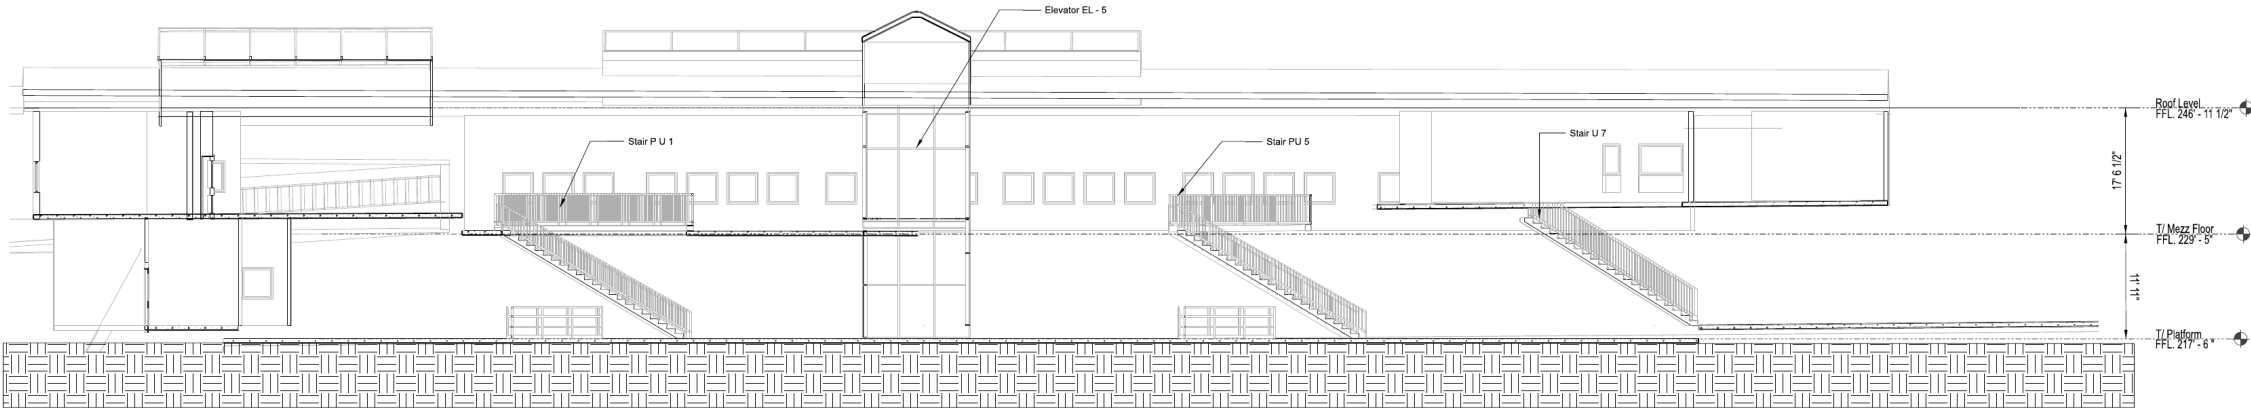

3 J/Z STATION - LONGITUDINAL SECTION
1/8" = 1'-0"

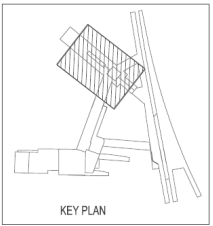

IT IS A VIOLATION OF THE PROFESSIONAL LICENSE LAW FOR ANY PERSON TO ALTER THIS DRAWING IN ANY WAY, UNLESS ACTING UNDER THE DIRECTION OF A LICENSED PROFESSIONAL ENGINEER / REGISTERED ARCHITECT. THE ALTERING ENGINEER/ARCHITECT SHALL AFFIX TO THE DRAWING HIS/HER SEAL AND THE NOTATION "ALTERED BY" FOLLOWED BY HIS/HER SIGNATURE AND THE DATE OF SUCH ALTERATION AND A SPECIFIC DESCRIPTION OF THE ALTERATION.

REVISION	DESCRIPTION	DATE	APPROVED
-	-	-	-
-	-	-	-
-	-	-	-
-	-	-	-





CONTRACT A37130
ADA UPGRADE OF BROADWAY JUNCTION STATION COMPLEX &
CIRCULATION IMPROVEMENTS, BOROUGH OF BROOKLYN

J/Z STATION SECTIONS

DRAWN BY	DEEPANSHU	15 FEBRAURY 2024	DATE: 15 FEBRAURY 2024
DESIGNED BY	WALDO MAFFEI	-	ARCHITECTURE
CHECKED BY	-	-	DRAWING NO: A37130_A-102001
APPROVED BY	-	-	REVISION

Section studies, J/Z Station

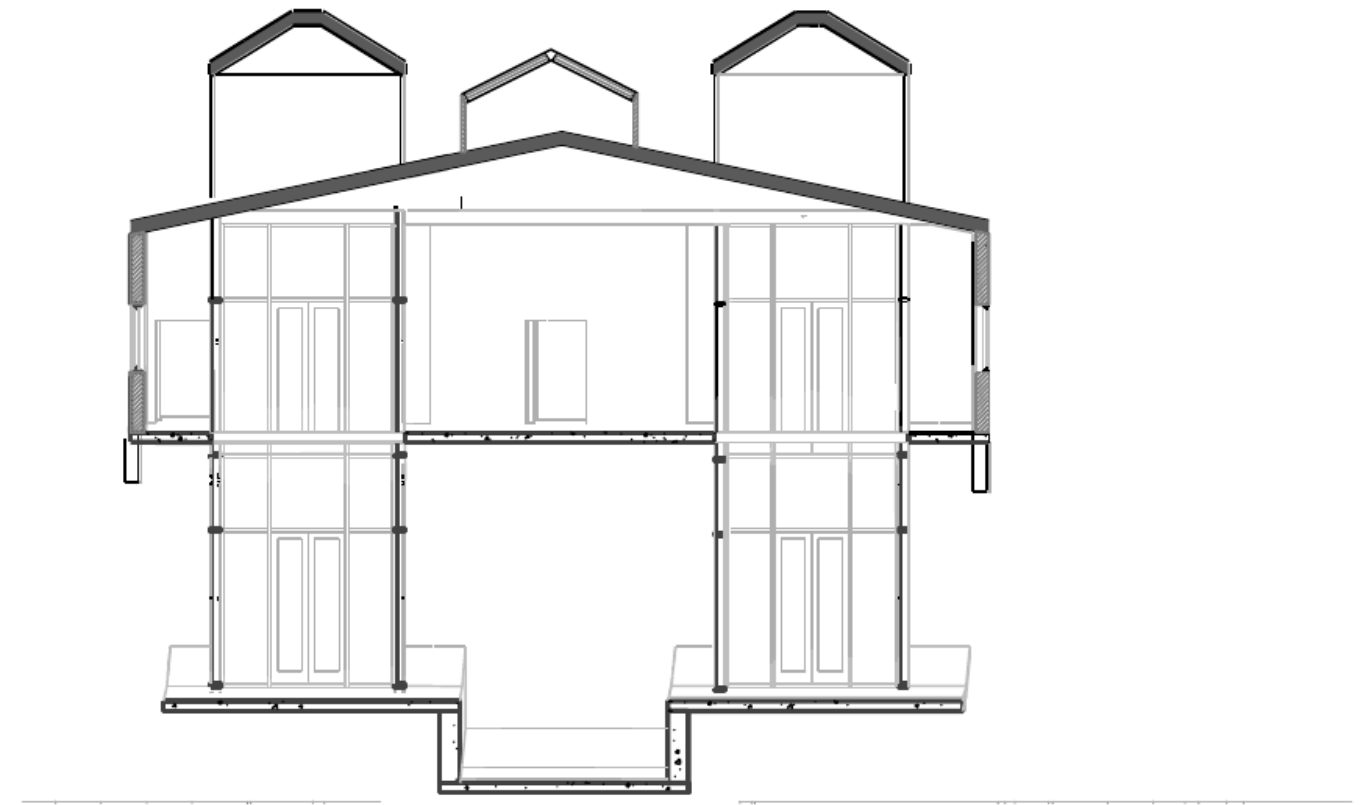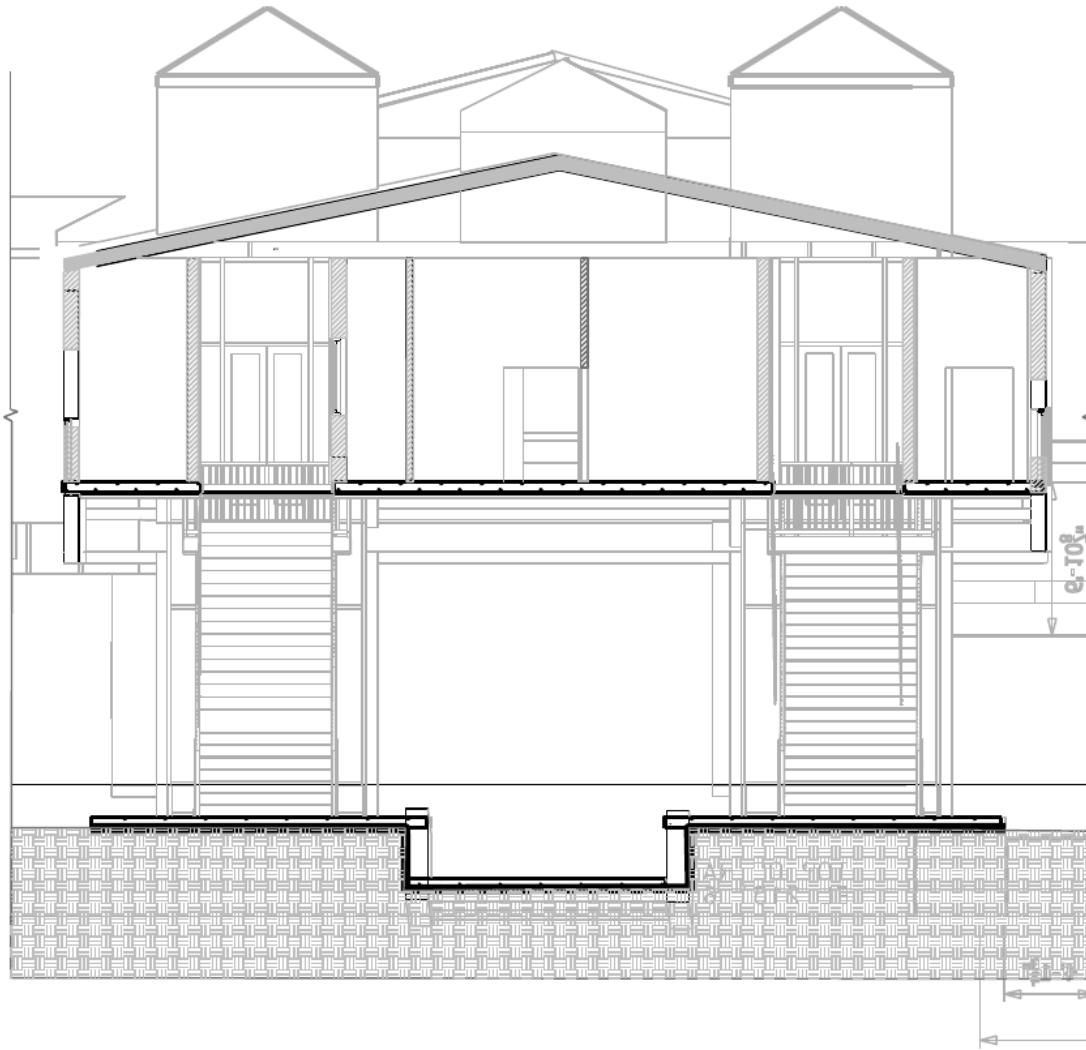

MY ROLE ON THE PROJECT

What I did

- Drafted plans and sections for the L and J/Z stations as part of the core architecture team.
- Coordinated design documentation day to day with the AtkinsRéalis team in the United States.
- Brought inputs from structure and other disciplines into one consistent drawing set.
- Checked the set against the technical and regulatory standards for public transport.

Residential and interior projects are available on request.

Renderings and drawings © AtkinsRéalis and MTA Construction & Development, shown here to illustrate my role on the project.

LET'S BUILD SOMETHING

Have a building in mind?

New projects, drawing sets that need care, or a team that needs one more pair of hands in BIM.

connect@deepanshujindal.com

deepanshujindal.com